

3.5. VERTINAMO TURTO FOTOFIKSACIJA







MATAVIMŲ CENTRAS

NEKILNOJAMOJO DAIKTO KADASTRINIŲ MATAVIMŲ BYLA

Tomas: 11

Nekilnojamojo turto objektas: Patalpa (butas)

Bylos Nr.: 13/14705

Registro Nr.: 44/1347448

Adresas: Vilniaus m. sav., Vilniaus m., Trinapolio g. 27-11

Lapų skaičius: 6

BYLOS TOMO VIDAUS APYRAŠAS

Eil. Nr.	Dokumento pavadinimas	Dokumento		Lapų sk.	Bylos lapų numeriai	Pastabos
		Nr.	data			
1	Patalpos(buto) planas	1	2010 02 02	2	1-2	
2	Patalpos(buto) kadastro duomenų forma 1D	2	2010 02 02	1	3	
3	Patalpos(buto) įkainojimo forma 2D	3	2010 02 02	1	4	
4	Pastato patalpų eksplikacija 3 forma	4	2010 02 02	1	5	

Matininkė

(pareigos)

2010 02 02

(data)


(parašas)

J. Puzinaitė


(v.pavadrė)





1014517341

COKOLINIS AUKŠTAS

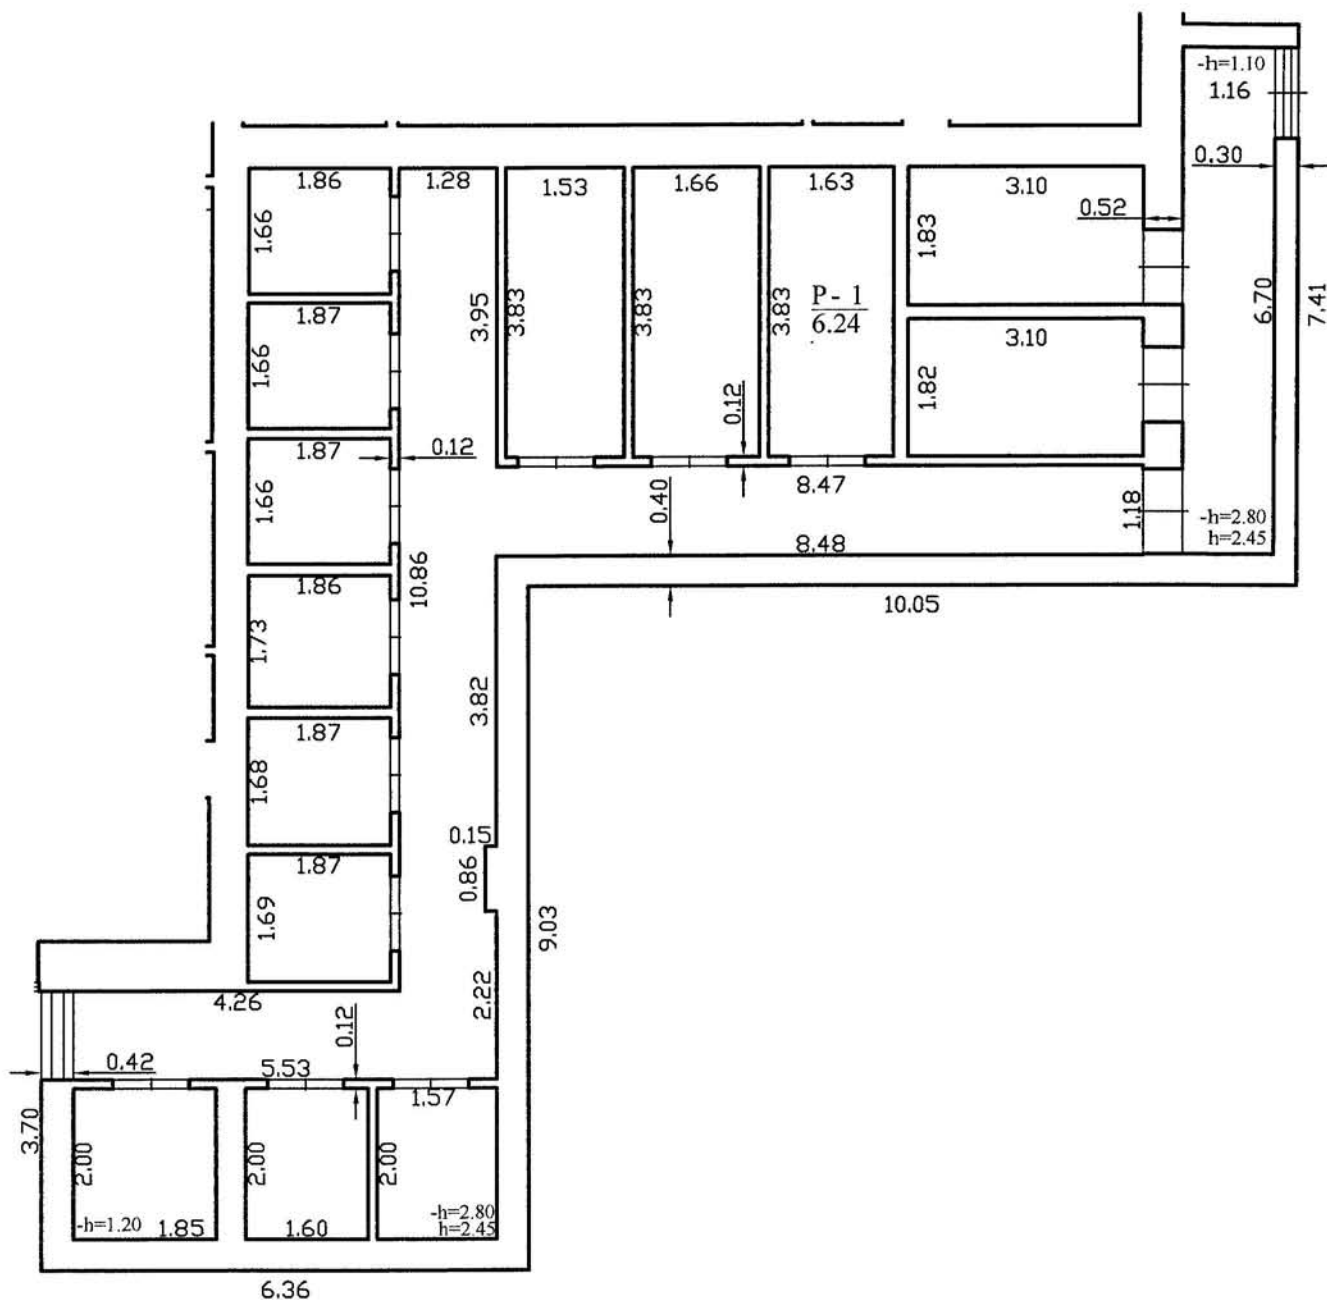


		UAB "Matavimų centras" Licencijos Nr.G-924-(1005), išduota 2008-11-12 Kvalifikacijos pažymėjimo Nr. 2M-M-574	
Pareigos	V., pavardė	Parašas	Data
matininkė	J.Puzinaitė		2010-02-02
Patalpų planas		1:100	A.V.
Vilniaus m. sav. Vilniaus m. Trinapolio g. 27			
Sudarytas pagal 2009-11-09 kadastrinių matavimų duomenis		Pastato pažymėjimas planas 23A3/m	



1014517341

ANTRAS AUKŠTAS

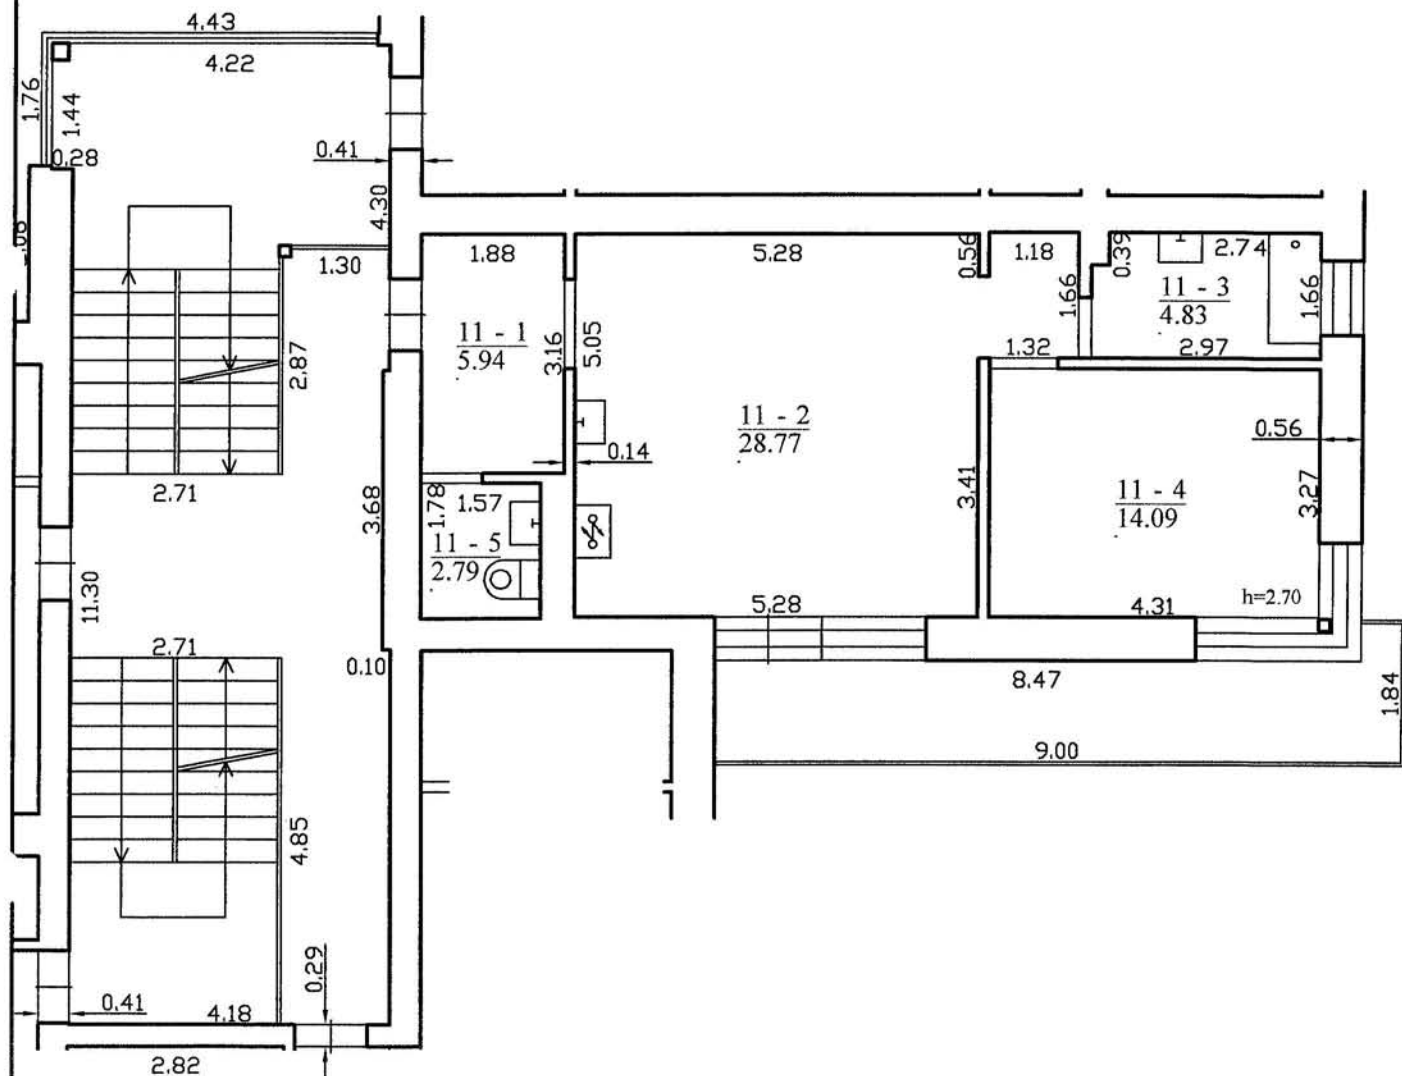

		UAB "Matavimų centras" Licencijos Nr.G-924-(1005), išduota 2008-11-12 Kvalifikacijos pažymėjimo Nr. 2M-M-574	
Pareigos	V., pavardė	Parašas	Data
matininkė	J.Puzinaitė		2010-02-02
11 Butas Buto planai		1:100	A.V.
Vilniaus m. sav. Vilniaus m. Trinapolio g. 27-11			
Sudarytas pagal 2009-11-09 kadastrinių matavimų duomenis		Pastato pažymėjimas planas 22A2/a	

Patalpos (buto) kadastro duomenys

Adresas Vilniaus m. sav. Vilniaus m. Trinapolio g. 27-11

Pavadinimas Butas

Aprašymas su sandėliuku 6,24 kv.m, pažymėtu P-1

Unikalus Nr. 4400-2020-6517:3184

Pažymėjimas plane 11

Paskirtis Gyvenamoji (butų)

Kad. duomenų nustatymo 2009-11-09

Patalpos (buto) kadastro duomenys

Aukštas:	2
Kambarių skaičius:	2
Bendras plotas: kv.m	56,42
Gyvenamasis plotas: kv.	42,86
Rūšys:	Yra
Baigtumo procentas: %	100
Karštas vanduo:	Yra

Šildymas:	Centrinis šildym. iš centr.
Vandentiekis:	Komunalinis vandentiekis
Nuotekų šalinimas:	Komunalinis nuotekų
Dujos:	Nėra
Viryklė:	Elektrinė
Vonios kambarys:	Yra

Pastato, kuriame yra butas (patalpa), duomenys

Pažymėjimas plane 23A3/p

Unikalus Nr. 1098-0014-3239

Paskirtis Gyvenamoji (3 ir daugiau butų)

Pavadinimas Daugiabutis gyvenamasis namas

Statybos pradžios metai:	1989
Statybos pabaigos metai:	1989
Baigtumo procentas: %	100
Koordinatė X:	6066528
Koordinatė Y:	583284

Rekonstravimo pradžios	2006
Rekonstravimo pabaigos	2009
Aukštų skaičius:	3
Tūris: kub.m	4245
Bendras plotas: kv.m	961,18

Parengė Matininkė Jolanta Puzinaitė




Patalpos (buto) įkainojimas (perkainojimas)

Adresas Vilniaus m. sav. Vilniaus m. Trinapolio g. 27-11
Unikalus Nr. 4400-2020-6517:3184

Vertės nustatymo data	(P)	Žymėjimas	Pavadinimas	Kasmetinis vertės mažinimo koeficientas	Matavimo vienetas	Kiekis	Kainynas ir lentelė	Vieneto statybos vertė po indeksavimo, Lt	Atkūrimo kaštai (statybinė vertė), Lt	Nusidėvėjimas %	Atkuriamoji vertė, Lt	Vietovės pataisos koeficientas	Vidutinė rinkos vertė, Lt
1	2	3	4	5	6	7	8	9	10	11	12	13	14
2010-02-02	1	11	Butas su sandėliuku	0.8	kv.m	56,42	Modelis: 5942	3297	186000	3	180000		141000

Parengė Matiminė Jolanta Puzinaitė



* 1 0 0 0 0 5 0 3 8 7 *

Lapas 1 iš 1

Patalpos (buto) vidaus plotų eksplikacija

Adresas Vilniaus m. sav. Vilniaus m. Trinapolio g. 27-11

Unikalus Nr. 4400-2020-6517:3184

Pavadinimas Butas

Žymėjimas 11

Paskirtis Gyvenamoji (buto)

Matavimų data 2009-11-09

Aukšto Nr.	Patalpos pažymėjimas plane		Patalpų pavadinimas	Gyvenamosios paskirties patalpų										Negyvenamosios paskirties patalpų	
	1 simbolis	2 simbolis		Bendras plotas m²	Naudingas plotas m²	Iš to skaičiaus			Pagalbinis nenaudingas plotas m²	Rūšių plotas m² (pusrūšių)	Garazų plotas m²	Pagrindinis plotas m²	Pagalbinis plotas m²		
						Gyvenamas plotas m²	Verslo plotas m²	Pagalbinis naudingas plotas m²							
1	2	3	4	5	6	7	8	9	10	11	12	13	14		
2	11	1	Koridorius	5,94	5,94			5,94							
2	11	2	Kambarys - virtuvė	28,77	28,77	28,77									
2	11	3	Sanitarinis mazgas	4,83	4,83			4,83							
2	11	4	Kambarys	14,09	14,09	14,09									
2	11	5	Sanitarinis mazgas	2,79	2,79			2,79							
Iš viso patalpų (5 patalpos)				56,42	56,42	42,86		13,56							
C	P	1	Sandėliukas 1\1 iš 6,24 kv.m	6,24						6,24					
Iš viso priklausinių (1 patalpos)				6,24						6,24					

Parengė Matininkė Jolanta Puzinaitė

2010-02-02

A.V.

