


3.5. VERTINAMO TURTO FOTOFIKSACIJA

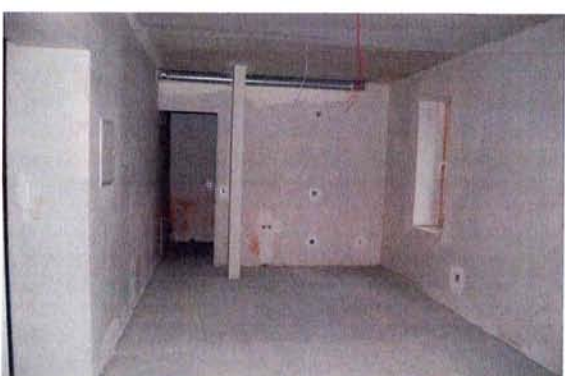





MATAVIMŲ CENTRAS

NEKILNOJAMOJO DAIKTO KADASTRINIŲ MATAVIMŲ BYLA

Tomas: **12**

Nekilnojamojo turto objektas: **Patalpa (butas)**

Bylos Nr.: **13/14705**

Registro Nr.: **44/1347447**

Adresas: **Vilniaus m. sav., Vilniaus m., Trinapolio g. 27-12**

Lapų skaičius: **6**

BYLOS TOMO VIDAUS APYRAŠAS

Eil. Nr.	Dokumento pavadinimas	Dokumento		Lapų sk.	Bylos lapų numeriai	Pastabos
		Nr.	data			
1	Patalpos(buto) planas	1	2010 02 02	2	1-2	
2	Patalpos(buto) kadastro duomenų forma 1D	2	2010 02 02	1	3	
3	Patalpos(buto) įkainojimo forma 2D	3	2010 02 02	1	4	
4	Pastato patalpų eksplikacija 3 forma	4	2010 02 02	1	5	

Matininkė

(pareigos)

2010 02 02

(data)


(parašas)

J. Puzinaitė


(v.pavadrė)





1014517440

COKOLINIS AUKŠTAS

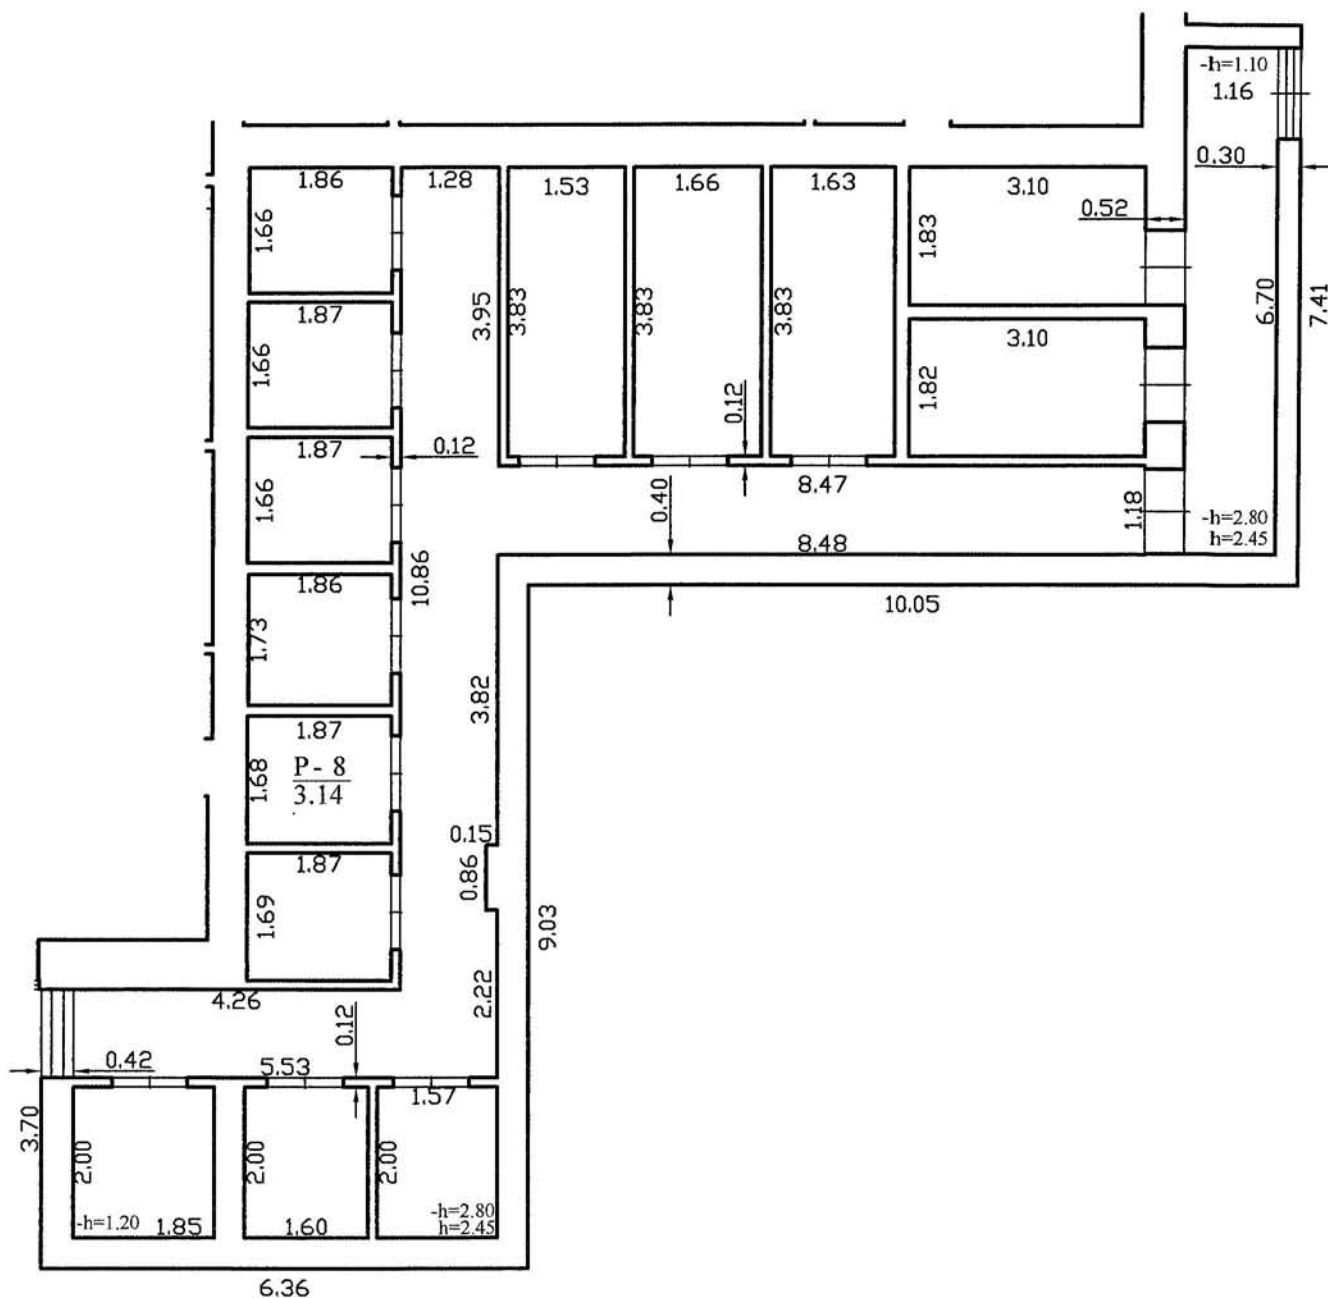


		UAB "Matavimų centras" Licencijos Nr.G-924-(1005), išduota 2008-11-12 Kvalifikacijos pažymėjimo Nr. 2M-M-574	
Pareigos	V., pavardė	Parašas	Data
matininkė	J.Puzinaitė		2010-02-02
Patalpų planas		1:100	A.V.
Vilniaus m. sav. Vilniaus m. Trinapolio g. 27			
Sudarytas pagal 2009-11-09 kadastrinių matavimų duomenis		Pastato pažymėjimas planas 23A2/a	



1014517440

ANTRAS AUKŠTAS

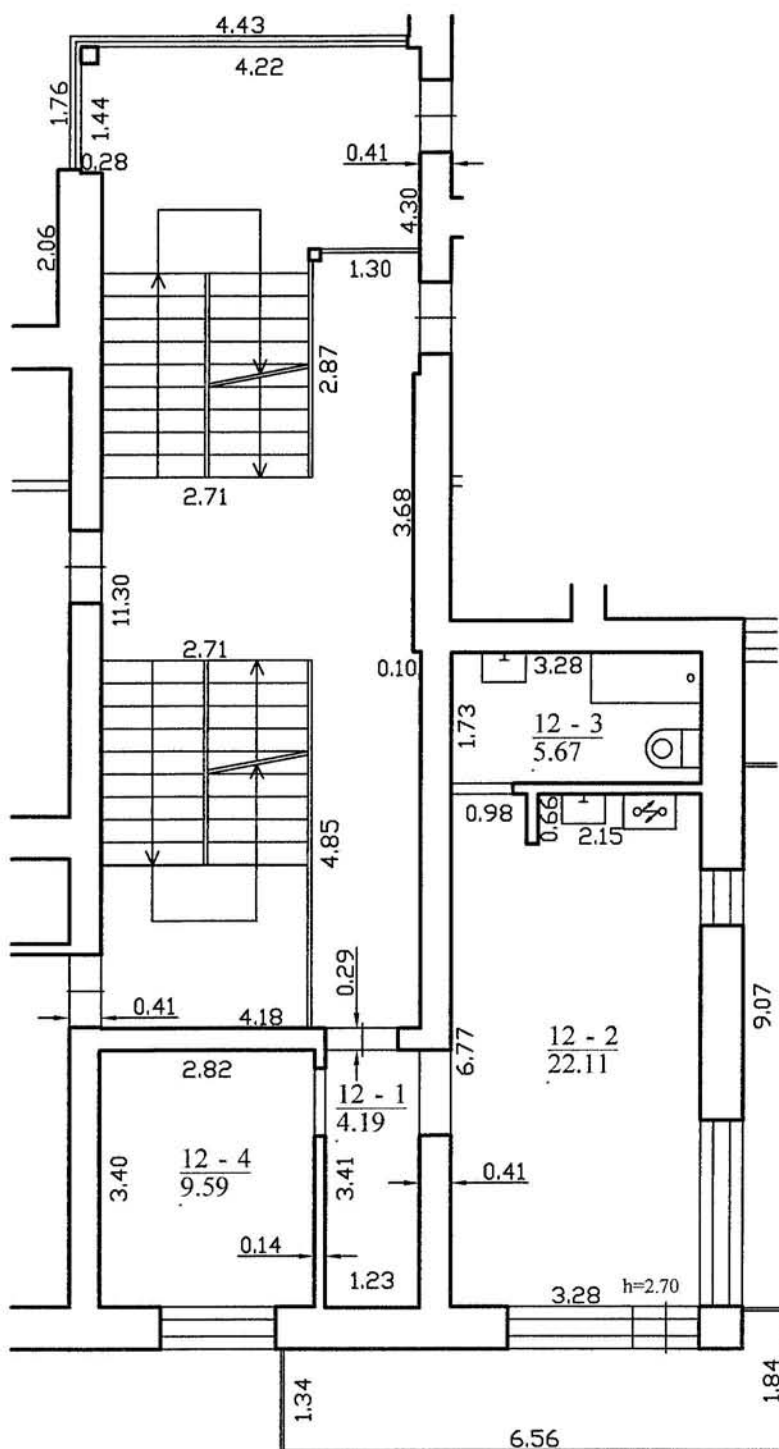

		UAB "Matavimų centras" Licencijos Nr.G-924-(1005), išduota 2008-11-12 Kvalifikacijos pažymėjimo Nr. 2M-M-574	
Pareigos	V., pavardė	Parašas	Data
matininkė	J.Puzinaitė		2010-02-02
12 Butas Buto planai		1:100	
Vilniaus m. sav. Vilniaus m. Trinapolio g. 27-12			
Sudarytas pagal 2009-11-09 kadastrinių matavimų duomenis		Pastato pažymėjimas plane 23A3/n	



Patalpos (buto) kadastro duomenys

Adresas Vilniaus m. sav. Vilniaus m. Trinapolio g. 27-12

Pavadinimas Butas

Aprašymas su sandėliuku 3,14 kv.m, pažymėtu P-8

Unikalus Nr. 4400-2020-6471:3183

Pažymėjimas plane 12

Paskirtis Gyvenamoji (butų)

Kad. duomenų nustatymo 2009-11-09

Patalpos (buto) kadastro duomenys

Aukštas:	2
Kambarių skaičius:	2
Bendras plotas: kv.m	41,56
Gyvenamasis plotas: kv.	31,7
Rūsų:	Yra
Baigtumo procentas: %	100
Karštas vanduo:	Yra

Šildymas:	Centrinis šildym. iš centr.
Vandentiekis:	Komunalinis vandentiekis
Nuotekų šalinimas:	Komunalinis nuotekų
Dujos:	Nėra
Viryklė:	Elektrinė
Vonios kambarys:	Yra

Pastato, kuriame yra butas (patalpa), duomenys

Pažymėjimas plane 23A3/p

Unikalus Nr. 1098-0014-3239

Paskirtis Gyvenamoji (3 ir daugiau butų)

Pavadinimas Daugiabutis gyvenamasis namas

Statybos pradžios metai:	1989
Statybos pabaigos metai:	1989
Baigtumo procentas: %	100
Koordinatė X:	6066528
Koordinatė Y:	583284

Rekonstravimo pradžios	2006
Rekonstravimo pabaigos	2009
Aukštų skaičius:	3
Tūris: kub.m	4245
Bendras plotas: kv.m	961,18

Parengė Matininkė Jolanta Puzinaitė





Patalpos (buto) įkainojimas (perkainojimas)

Adresas Vilniaus m. sav. Vilniaus m. Trinapolio g. 27-12
Unikalus Nr. 4400-2020-6471:3183

Vertės nustatymo data	(P)	Žymėjimas	Pavadinimas	Kasmetinis vertės mažinimo koeficientas	Matavimo vienetas	Kiekis	Kainynas ir lentelė	Vieneto statybos vertė po indeksavimo, Lt	Atkūrimo kaštai (statybinė vertė), Lt	Nusidėvėjimas %	Atkuriamoji vertė, Lt	Vietovės patalpos koeficientas	Vidutinė rinkos vertė, Lt
1	2	3	4	5	6	7	8	9	10	11	12	13	14
2010-02-02	1	12	Butas su sandėliuku	0.8	kv.m	41,56	Modelis: 5942	3297	137000	3	133000		109000

Parengė Matininkė Jolanta Puzinaite

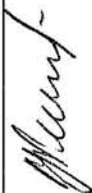


Patalpos (buto) vidaus plotų eksplikacija

Adresas Vilniaus m. sav. Vilniaus m. Trinapolio g. 27-12

Unikalus Nr. 4400-2020-6471:3183

Žymėjimas 12

Pavadinimas Butas


Paskirtis Gyvenamoji (butų)

Matavimų data 2009-11-09

Aukšto Nr.	Patalpos pažymėjimas plane		Patalpų pavadinimas	Gyvenamosios paskirties patalpų								Negyvenamosios paskirties patalpų	
	1 simbolis	2 simbolis		Bendras plotas m ²	Naudingas plotas m ²	Gyvenamas plotas m ²	Iš to skaičiaus	Pagalbinis naudingas plotas m ²	Pagalbinis nenaudingas plotas m ²	Rūšių (pusrūšių) plotas m ²	Garazų plotas m ²	Pagrindinis plotas m ²	Pagalbinis plotas m ²
1	2	3	4	5	6	7	8	9	10	11	12	13	14
2	12	1	Koridorius	4,19	4,19			4,19					
2	12	2	Kambarys - virtuvė	22,11	22,11	22,11							
2	12	3	Sanitarinis mazgas	5,67	5,67			5,67					
2	12	4	Kambarys	9,59	9,59	9,59							
Iš viso patalpų (4 patalpos)				41,56	41,56	31,70		9,86					
C	P	8	Sandėliukas 1\1 iš 3,14 kv.m	3,14						3,14			
Iš viso priklausinių (1 patalpos)				3,14						3,14			

Parengė Matininkė Jolanta Puzinaitė

2010-02-02 A.V.

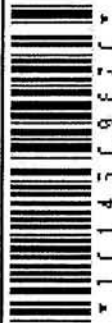

1 1 1 1 4 5 0 9 8 7 0